



Hand-drawn floor plan of a two-unit residential building. The plan shows two units, Unit #1 and Unit #2, separated by a central hallway labeled "WALKWAY".

- Unit #1 (Top Right):** Includes a Living Room, Kitchen, and Bathroom. It has a patio labeled "PATIO #1".
- Unit #2 (Bottom Left):** Includes a Living Room, Bedroom, and Bathroom. It has a patio labeled "PATIO #2".

Dimensions are noted: 23'-0" for the overall width and 23'-0" for the depth of Unit #2. A large, bold, black "ARC" is overlaid on the right side of the plan.


2021-2026

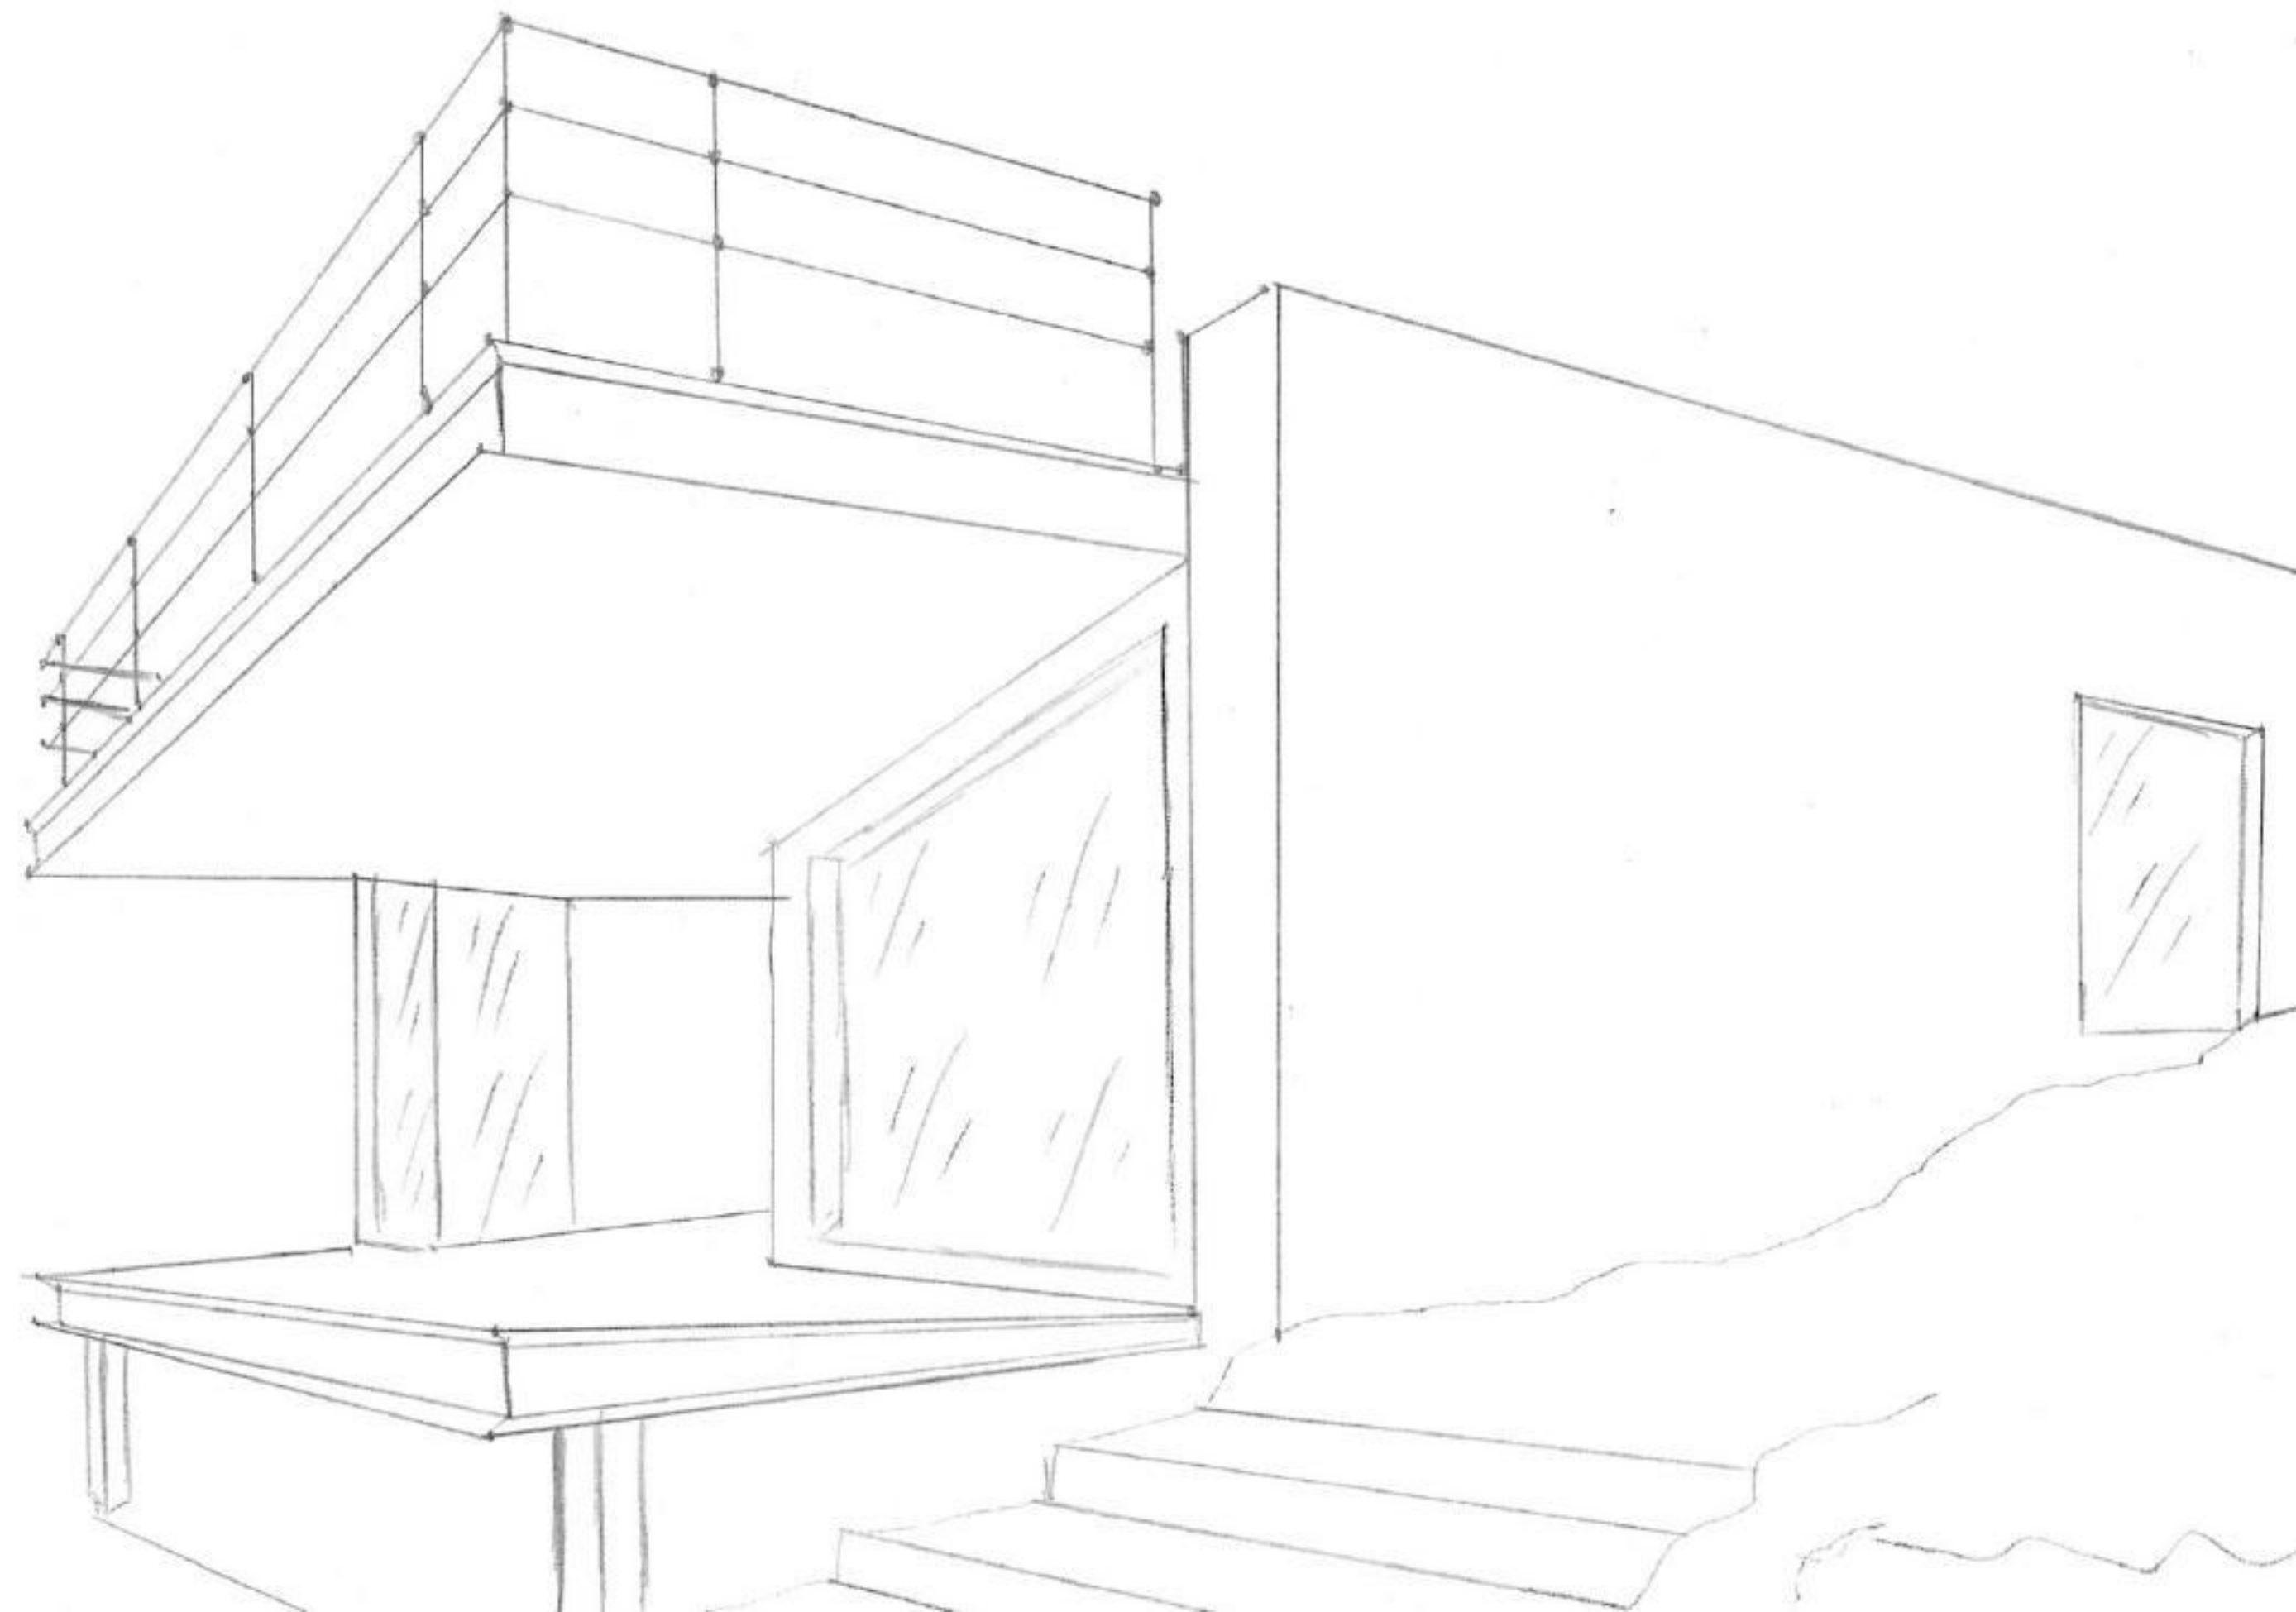

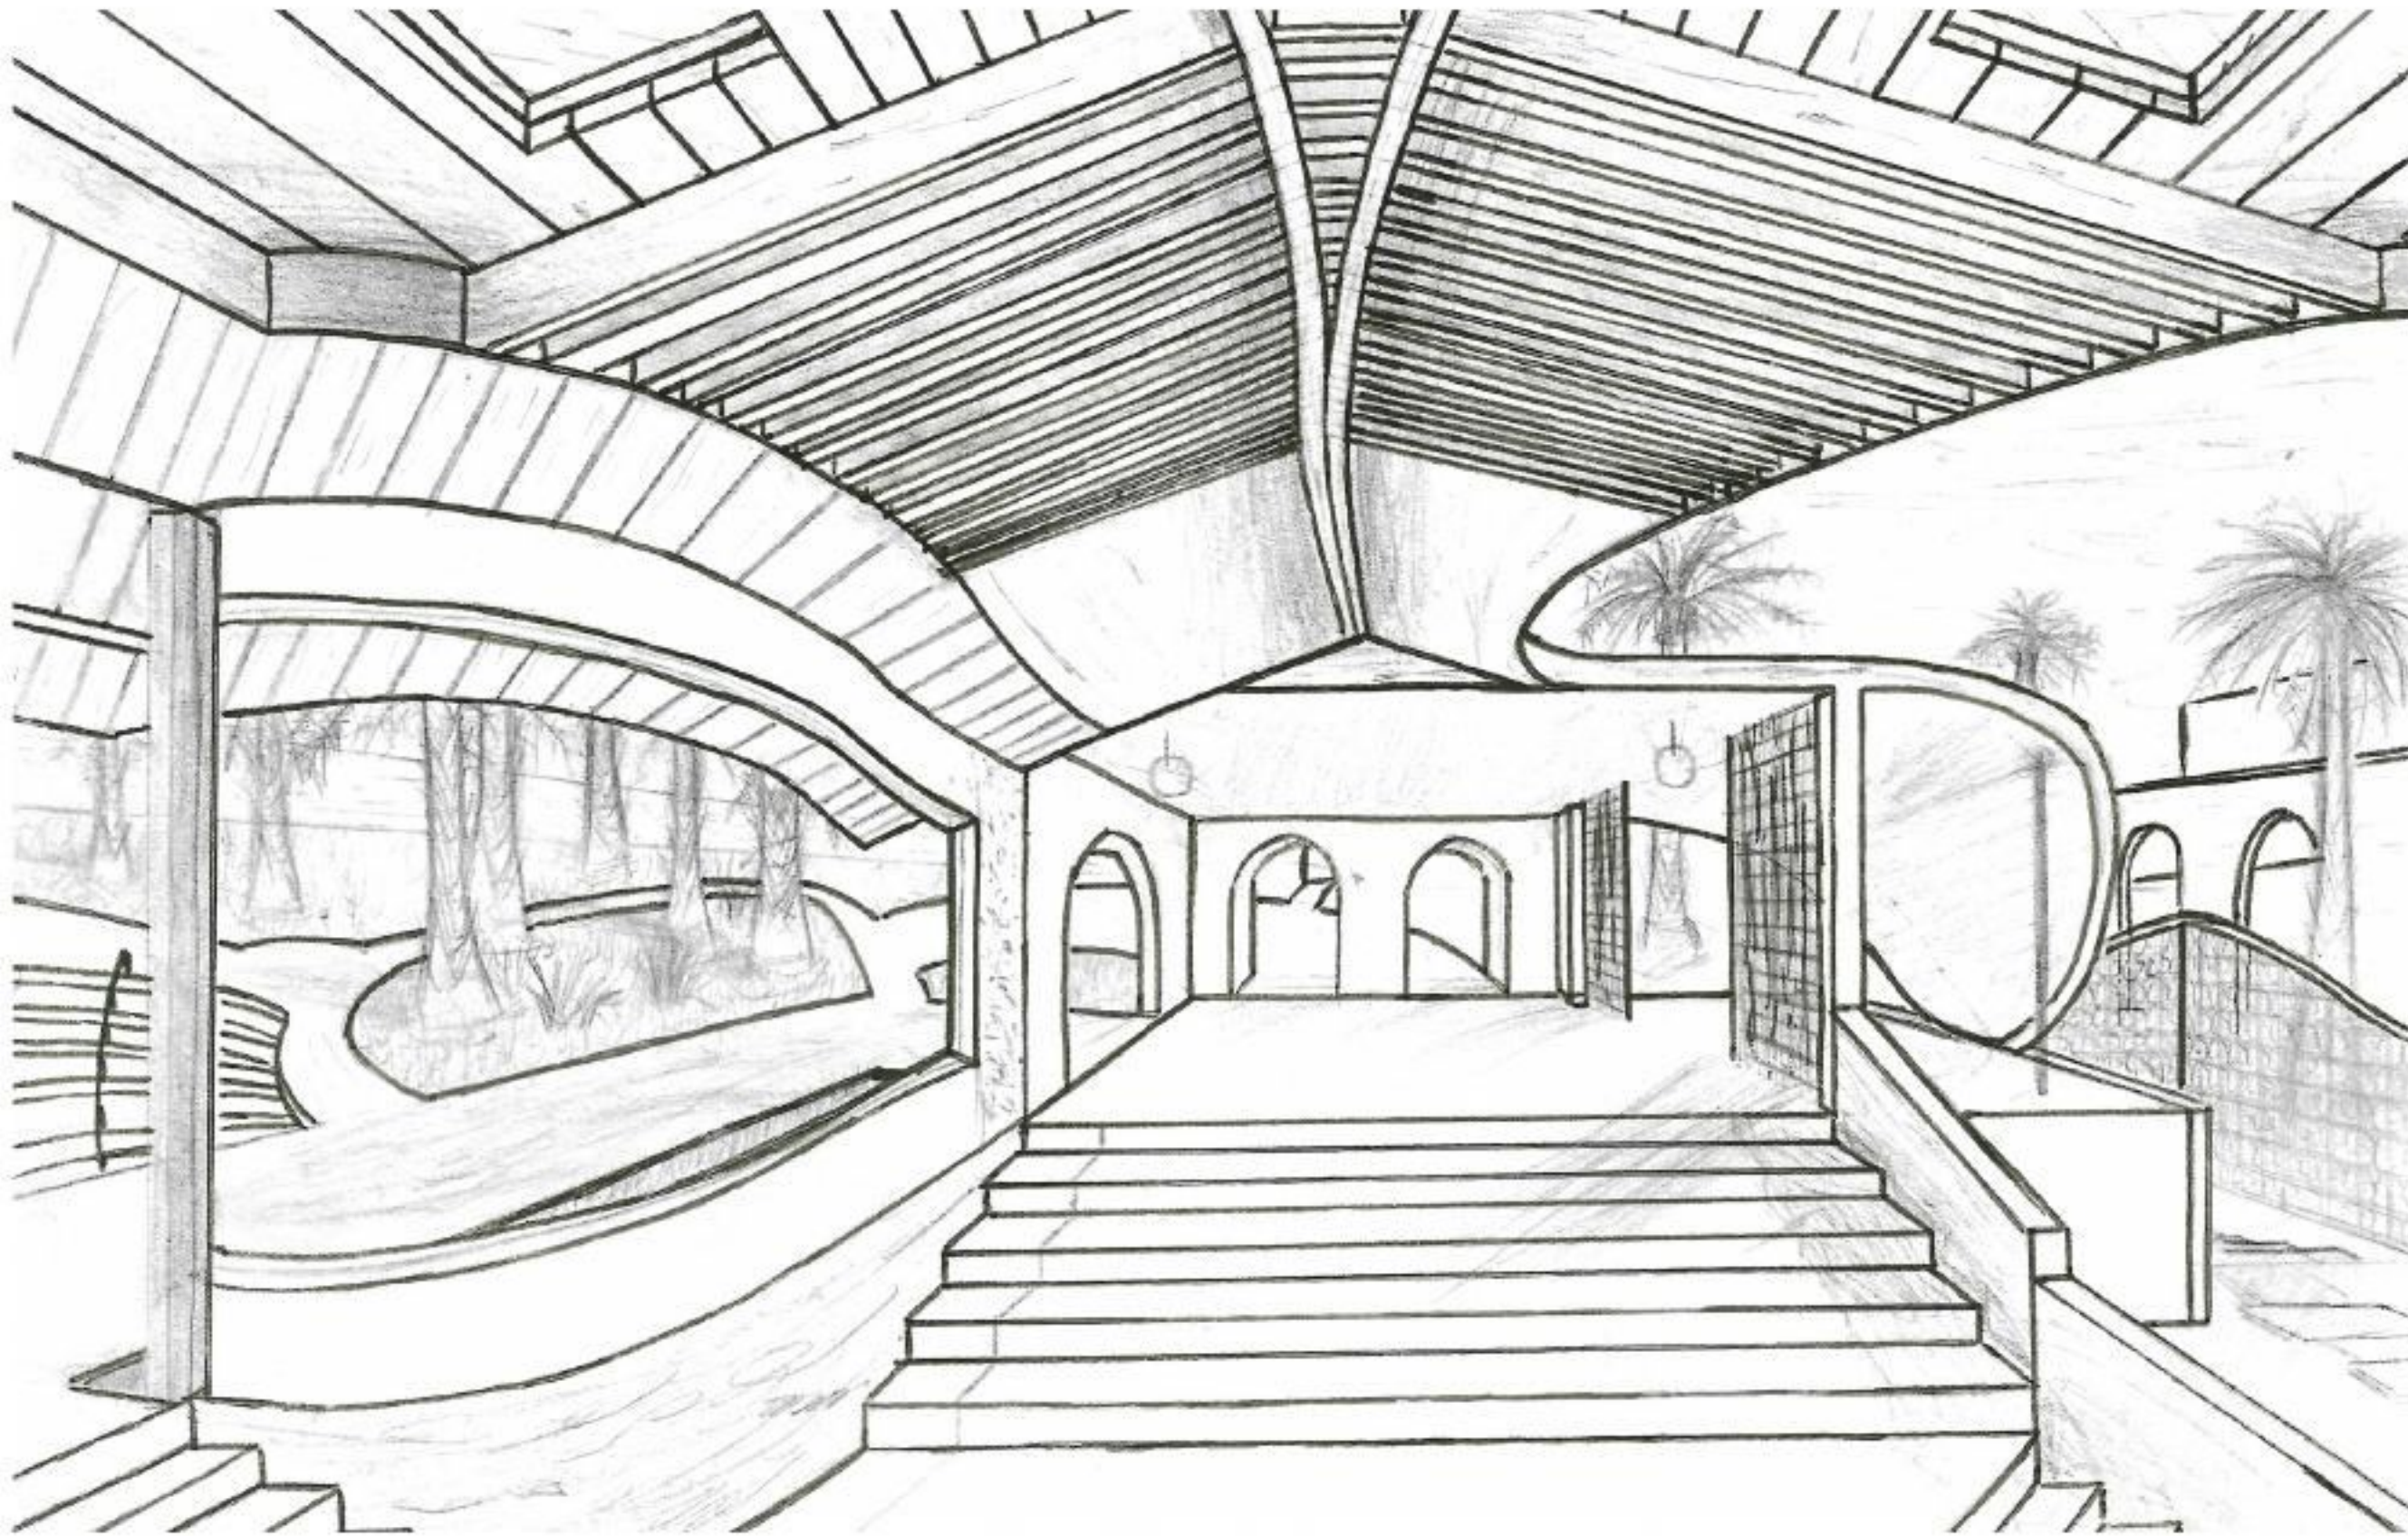


INTERIOR TROPICAL PERSPECTIVE, AUGUST, 2025
PEN AND PENCIL ON PAPER
5" X 7"


ARCHITECTURAL INTERIOR SKETCHING

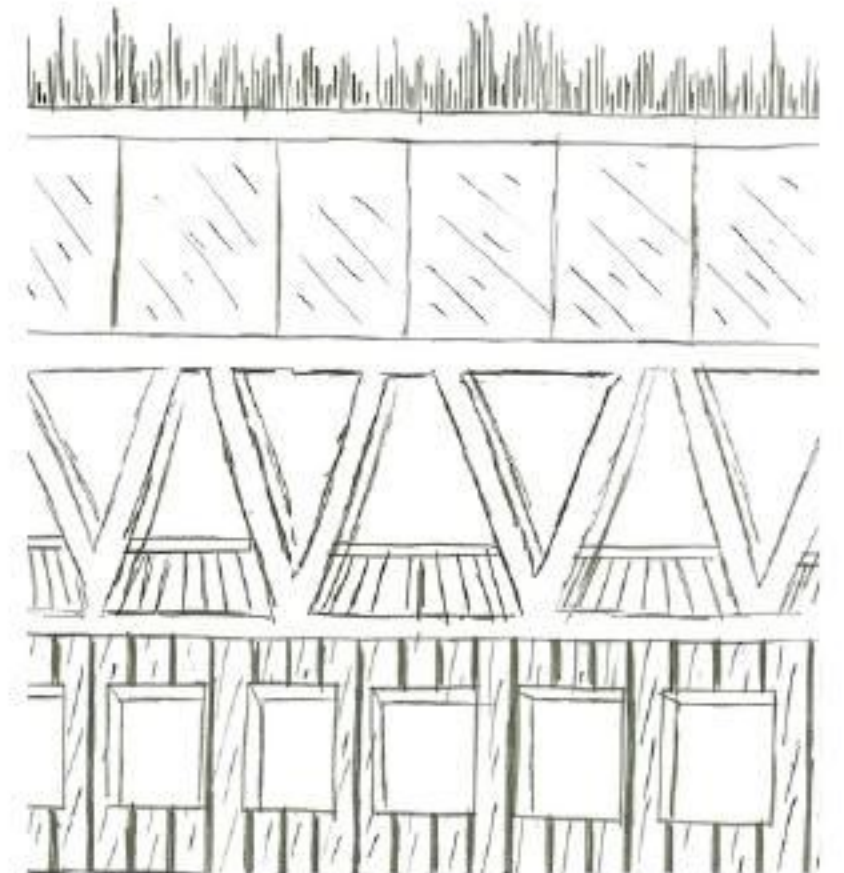

INTERIOR FACADE STUDY
JANUARY, 2024
PEN AND PENCIL ON PAPER
5" X 7"

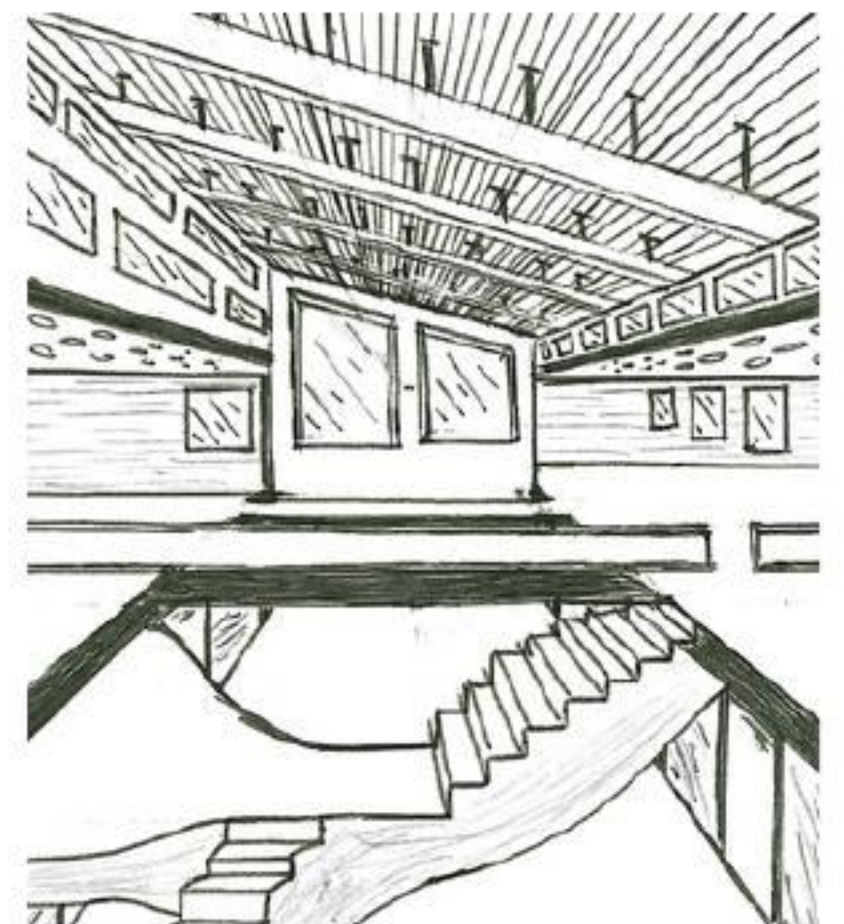


MUSEUM HALLWAY
JANUARY, 2024
PEN AND PENCIL ON PAPER
5" X 7"


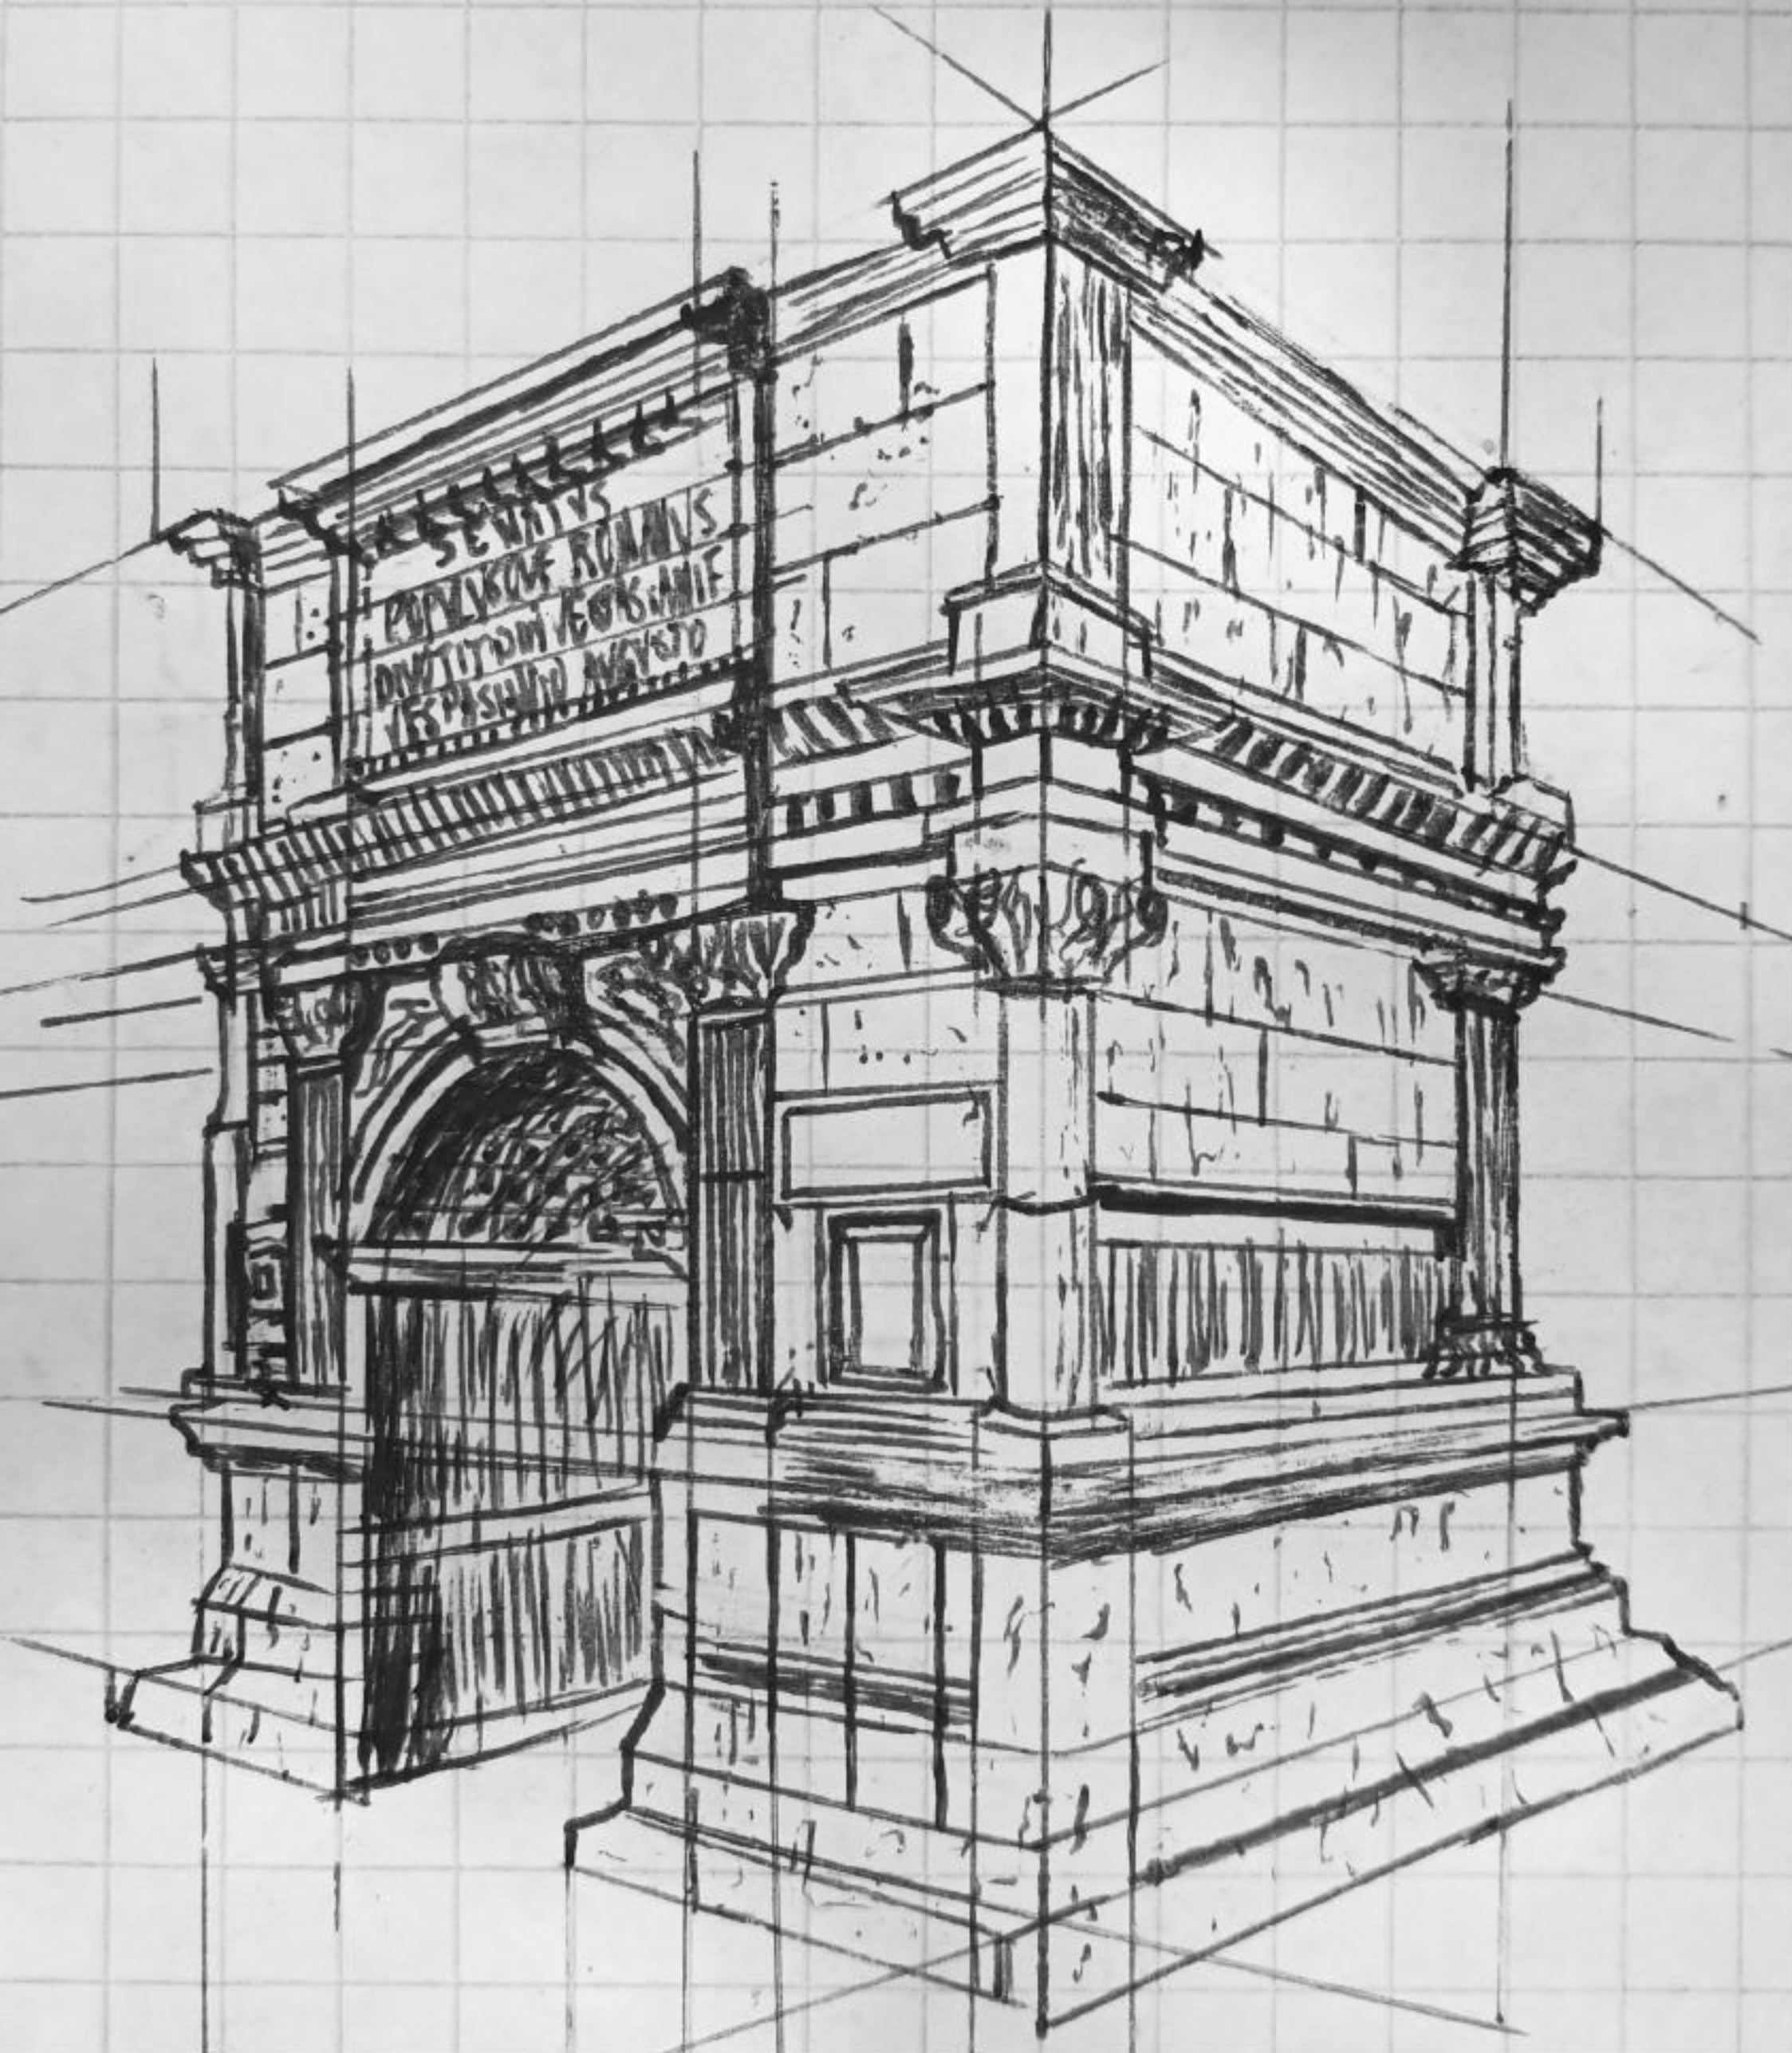


**ARCH OF TITUS PERSPECTIVE SKETCH
PEN ON PAPER
4" X 5"**

OBSERVATIONAL SKETCHES

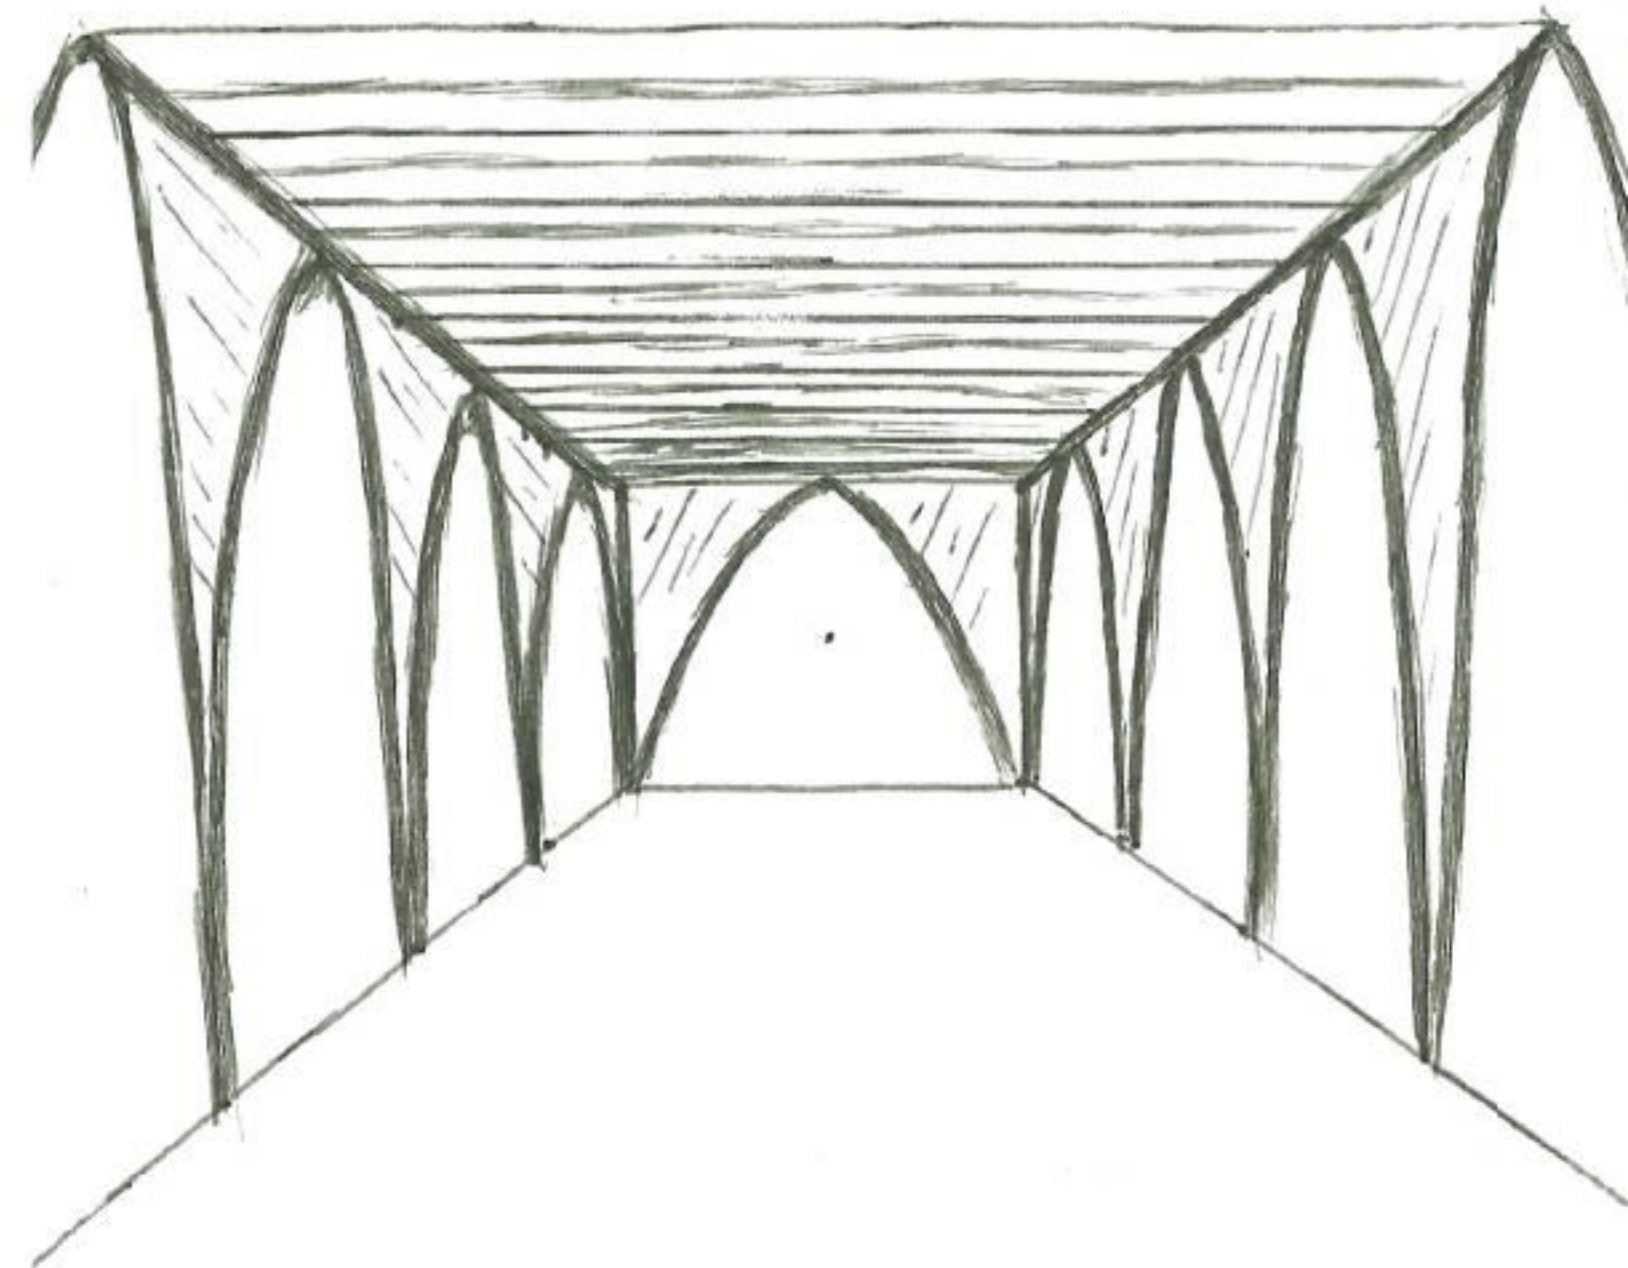


**DENVER BOTANICAL GARDENS OBSERVATION
PEN AND PENCIL ON PAPER
5" X 7"**

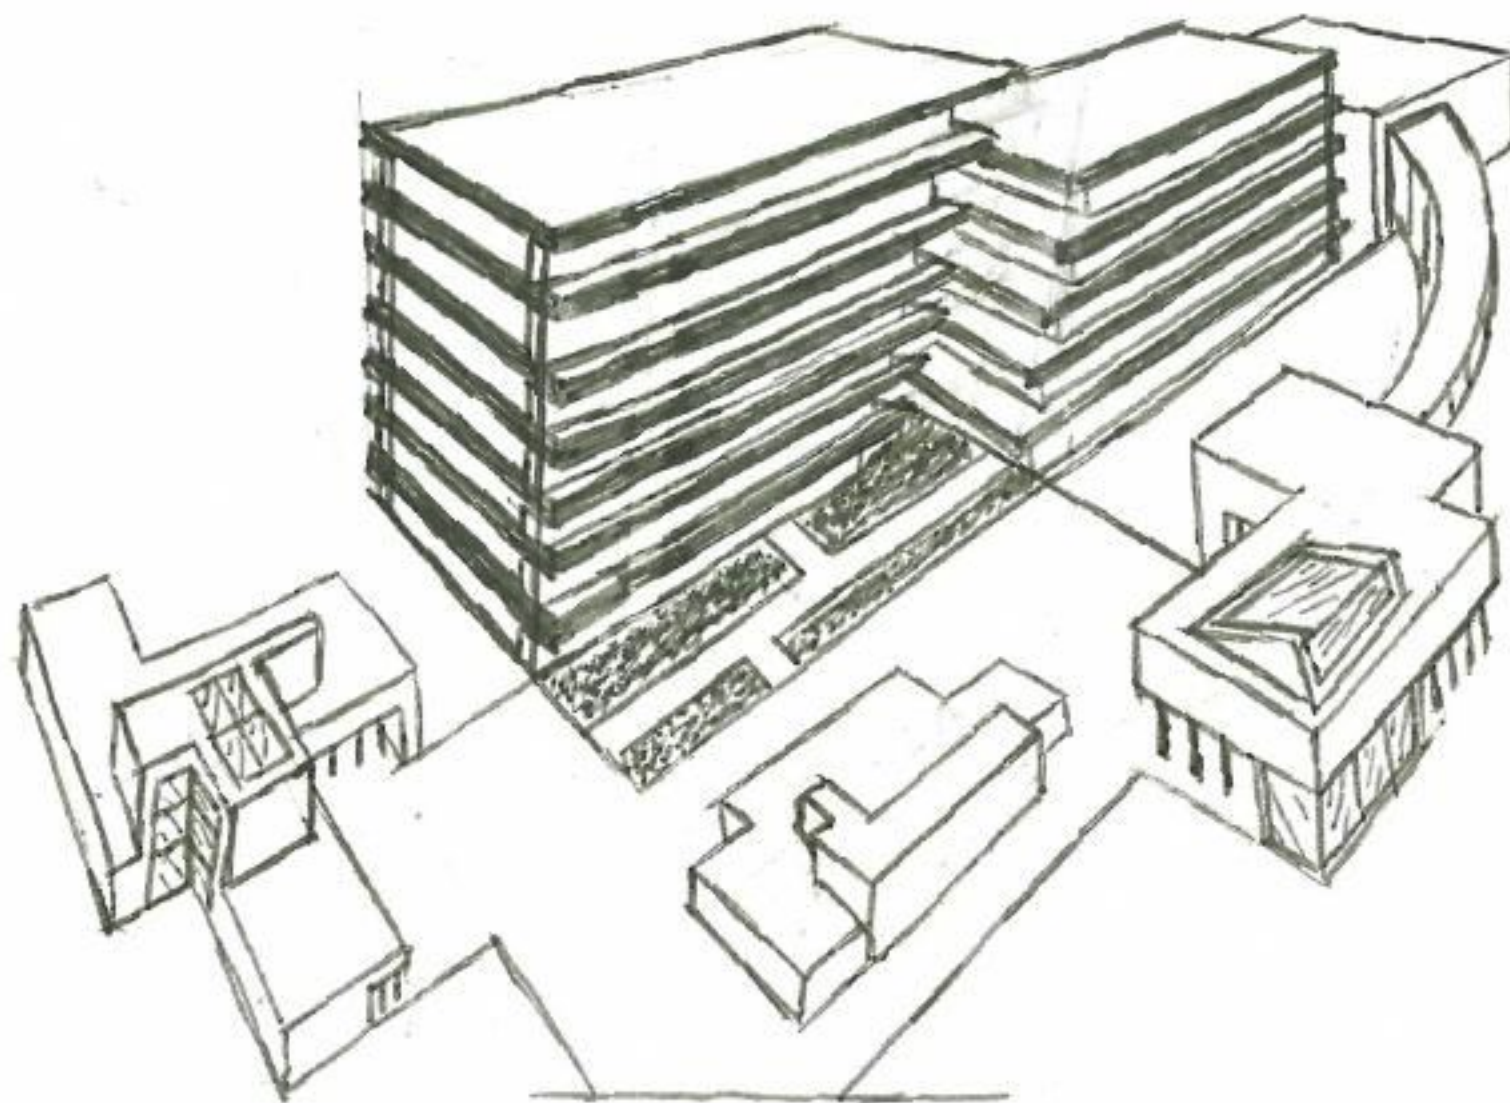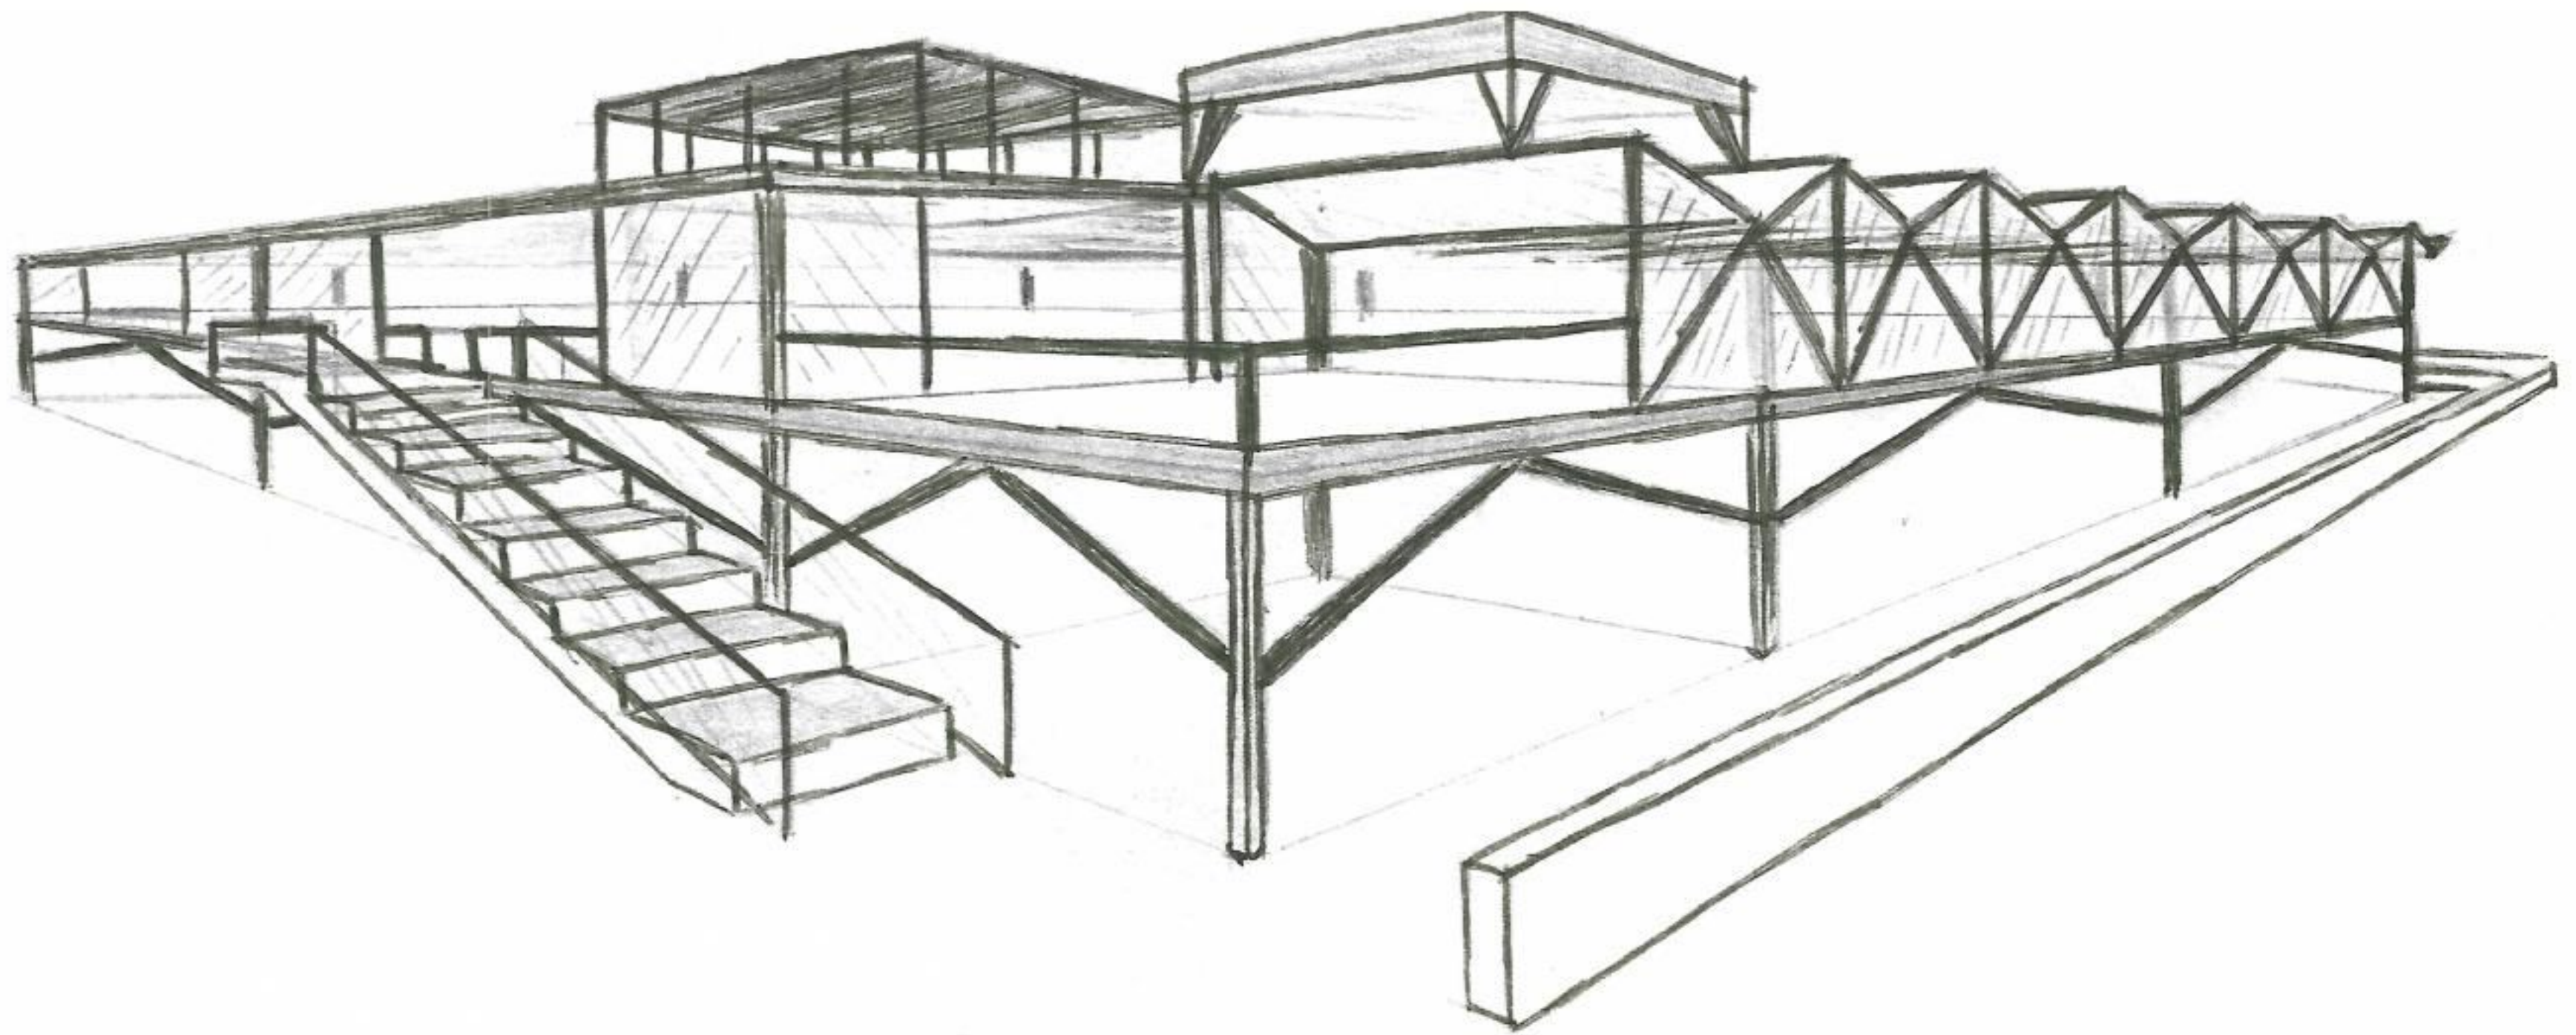

DESIGN SKETCHES

These sketches show some of my drawings depicting personal designs and explorations of form and shape. The top image is a drawing of a bare framework-style design. The bottom image shows a potential neighborhood or community area. Both are studies in developing sketches from pure imagination and seeking inspiration for future projects.

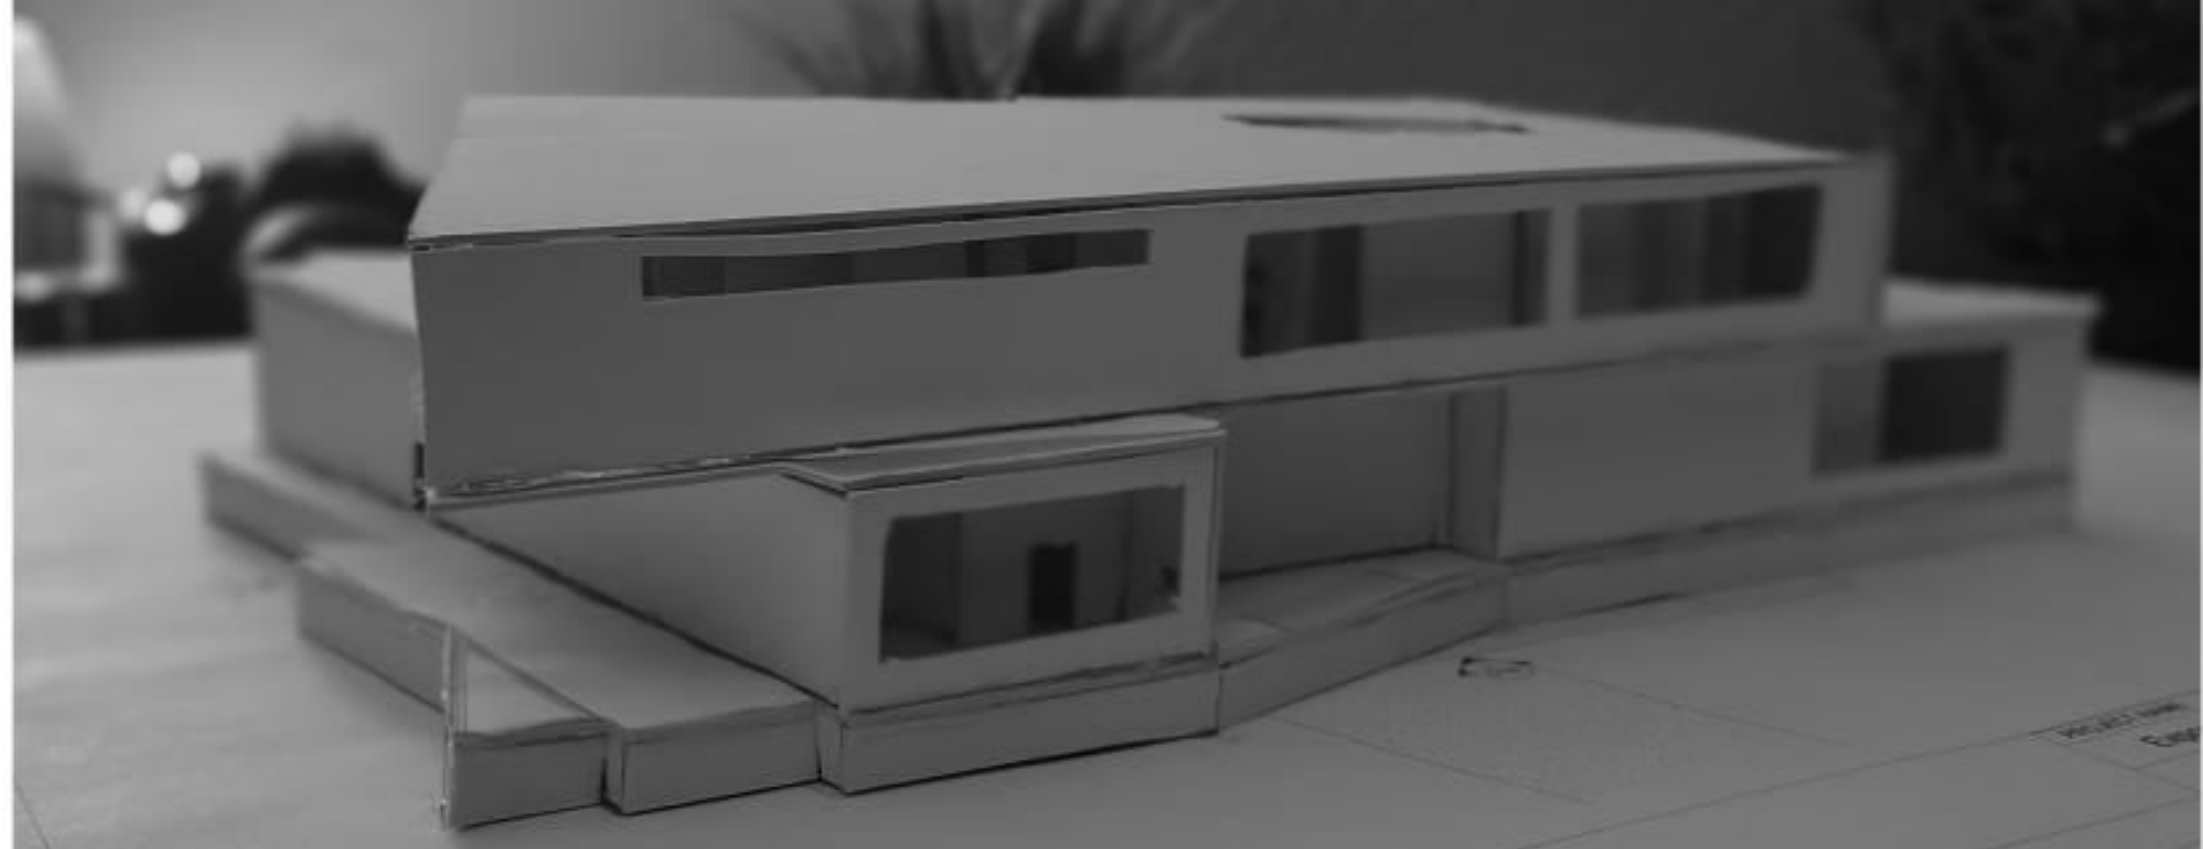

EXPOSICION DE ARTE MODERNO: MODEL


This project was of a contemporary, somewhat brutalist art museum for Mexico City. I made several sketches, a digital model, and these physical models. The images show the entrance portal to the museum, a front/right profile view, and a bird's-eye view of the 2nd floor courtyard.

SINGAPORE PERFORMING ARTS CENTER PROJECT

This project was created for submission the Davidson Fellows scholarship.. The design principle I explored with this building was creating a curvilinear, organic form that incorporated natrual/green spaces, along with LEED strategies and clean materials.



MODEL-MAKING PROCESS PHOTO
JANUARY, 2026
PEN ON PAPER

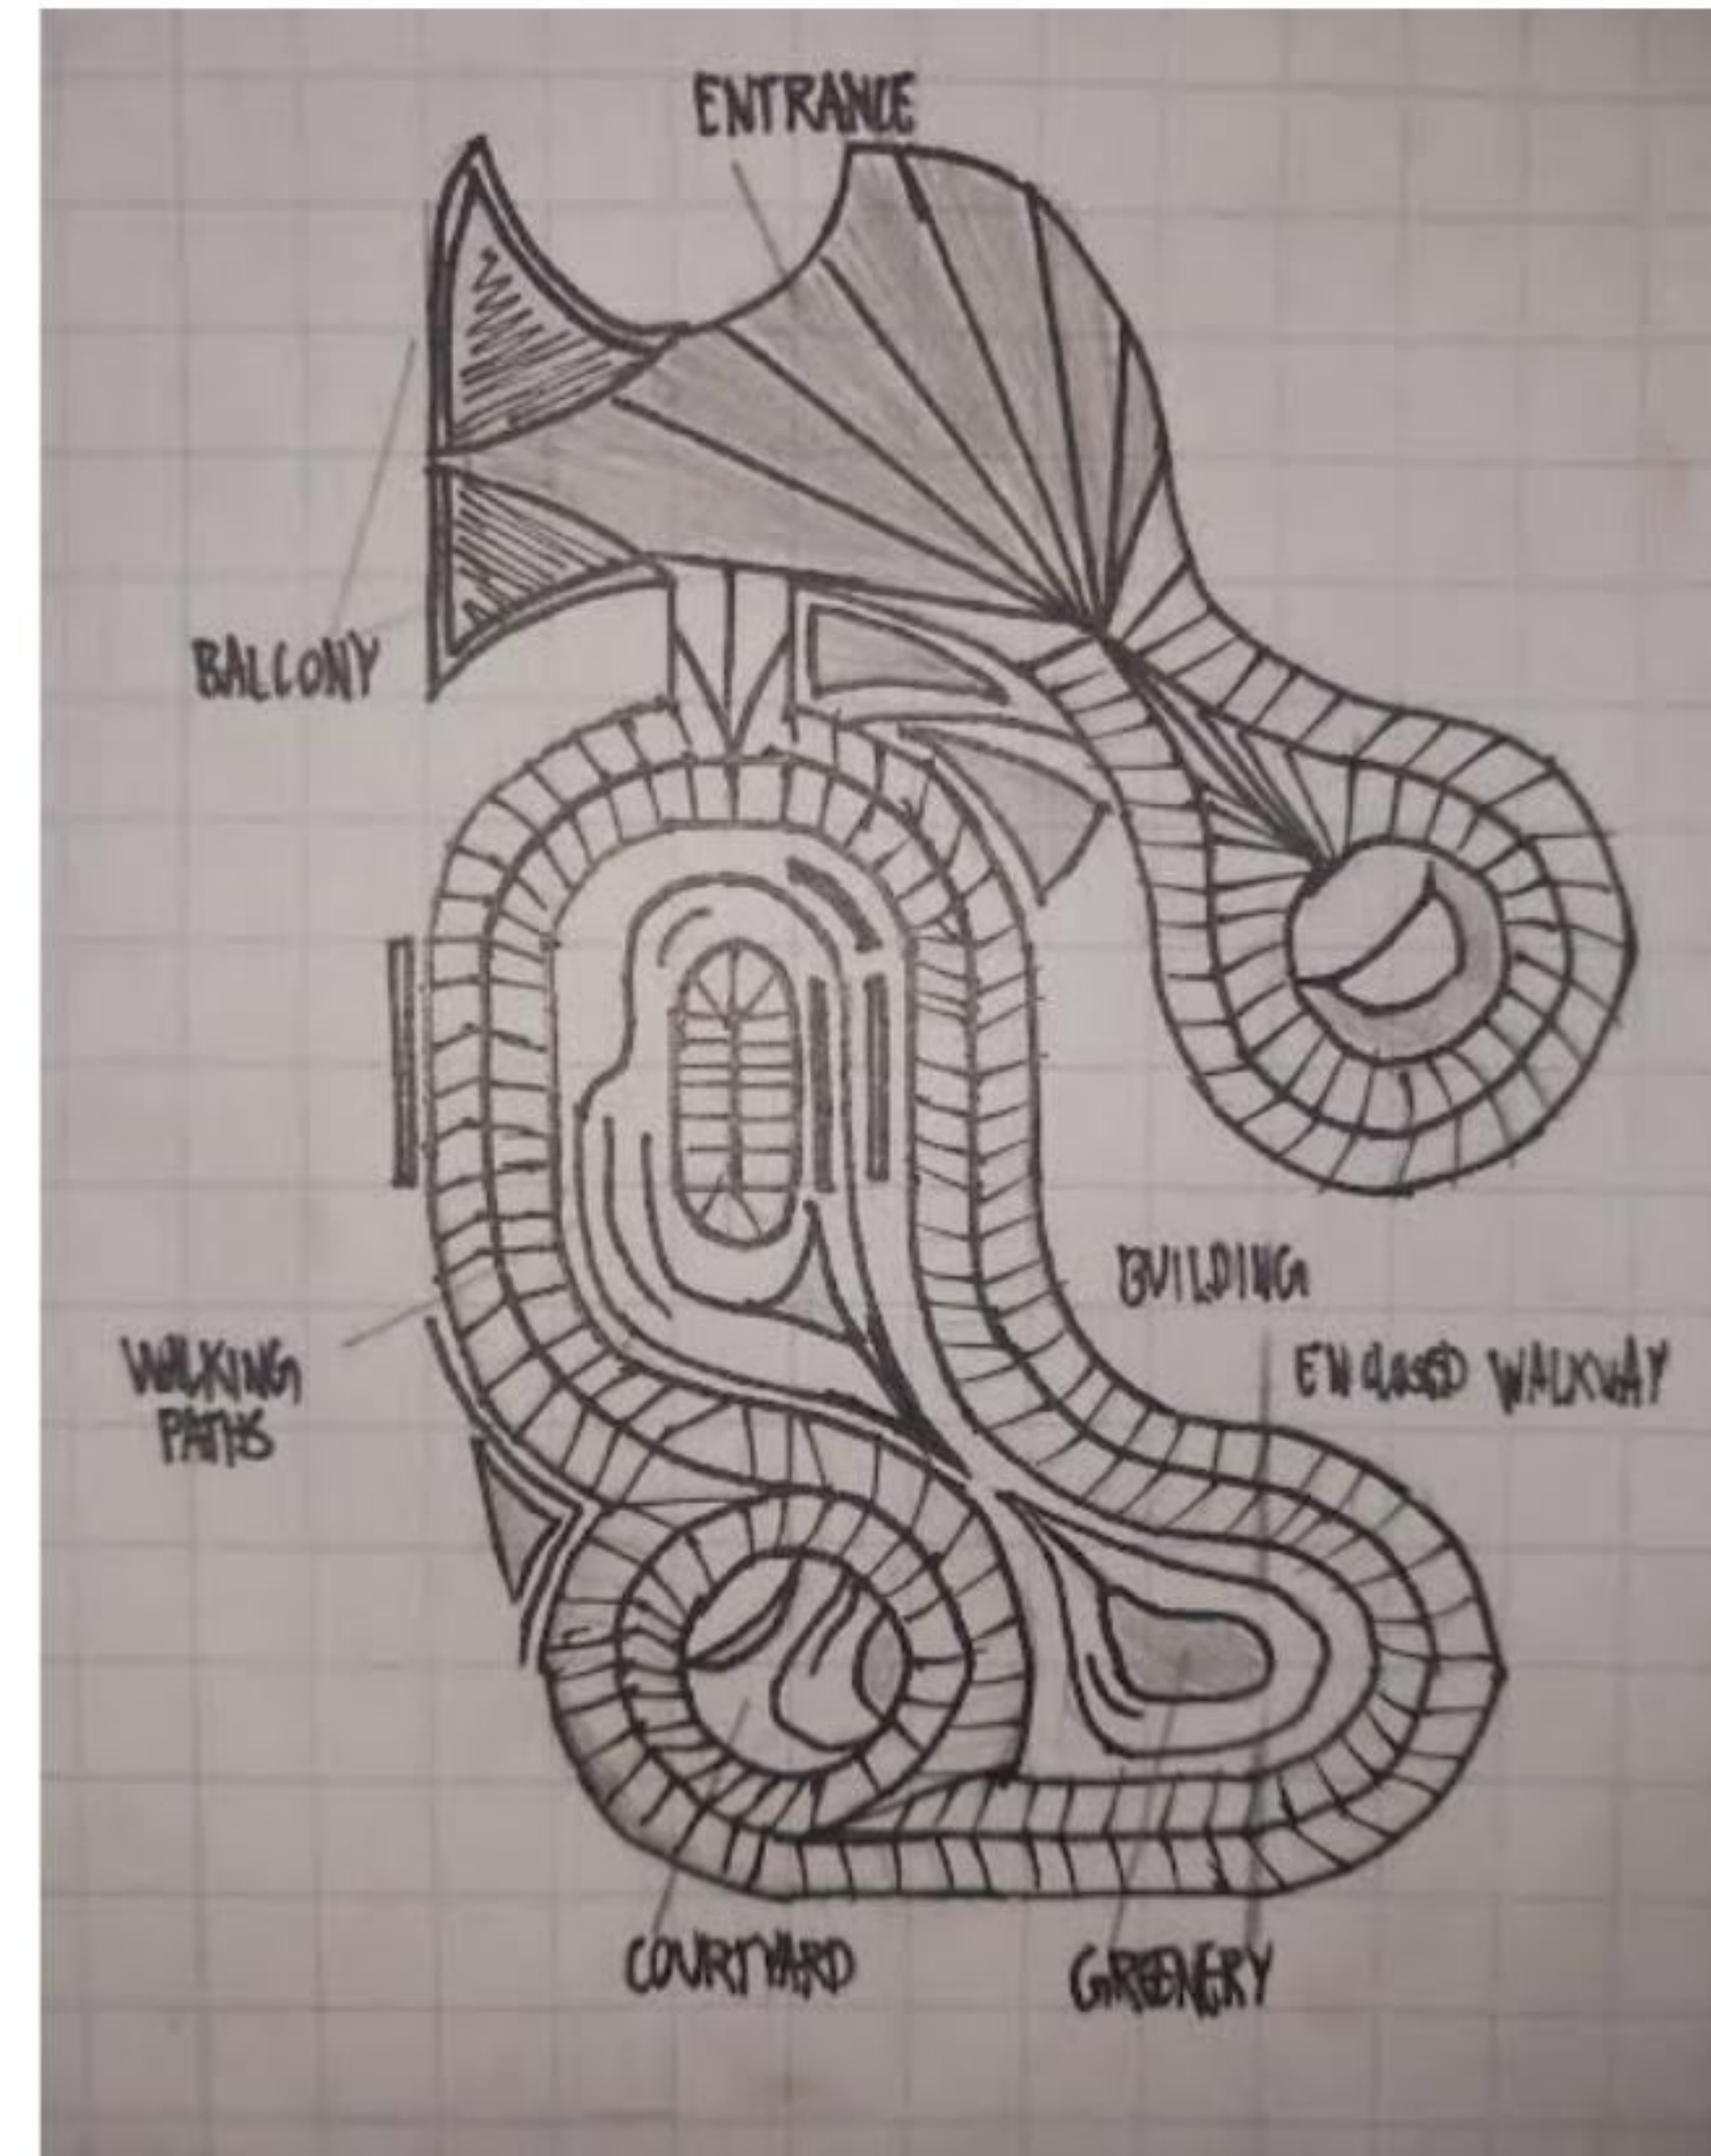

FACADE PHOTOGRAPHY



Populus Hotel, Denver Facade

This hotel facade features a very unique facade, with many eye-shaped windows. This caught my eye for its design, so I decided to capture an image of this building.

June, 2025. Digital Photograph



POST, Houston Facade

This public, community space in Houston, Texas is very interesting to me for its use of this former USPS warehouse for hosting car shows, art shows, and cultural and artistic events. The facade of this building, in particular, stuck out to me for its repeated pattern and subtle design.

December, 2025. Digital Photograph



OLD FAITHFUL INN INTERIOR
JUNE, 2025
DIGITAL PHOTOGRAPH

INTERIOR ARCHITECTURE PHOTOGRAPHY



POST, HOUSTON INTERIOR MATERIAL STUDY
DECEMBER, 2025
DIGITAL PHOTOGRAPH



BUILDING STRUCTURE DETAIL
JUNE, 2025
DIGITAL PHOTOGRAPH